SULTANATE OF OMAN
MINISTRY OF AGRICULTURE, FISHERIES WEALTH AND WATER RESOURCES

FLOOD PROTECTION SCHEME IN NORTH AND SOUTH AL BATINAH GOVERNORATES BLOCK 04

PLAN AND PROFILE DRAWINGS OF THE FLOOD PROTECTION CHANNELS

Hydraulic design for the 200-year return period

Design stage: Flood Protection Channel

Drawing set 2224-PD-HY-PP-B4

Revision 1 11.10.2026

RENARDET S.A. & PARTNERS
Consulting Engineers LLC.

TABLE OF DRAWINGS

No.	Drawing No.	Catchment	Channel	Drawing	Station from	Station to	Page
1	2224-PD-HY-PP-B4-001	Al Hawasinah	HAW-CH1-FP	Key map			5
2	2224-PD-HY-PP-B4-002	Al Hawasinah	HAW-CH1-FP	Sheet 1 of 9	0+000	1+000	6
3	2224-PD-HY-PP-B4-003	Al Hawasinah	HAW-CH1-FP	Sheet 2 of 9	1+000	2+000	7
4	2224-PD-HY-PP-B4-004	Al Hawasinah	HAW-CH1-FP	Sheet 3 of 9	2+000	3+000	8
5	2224-PD-HY-PP-B4-005	Al Hawasinah	HAW-CH1-FP	Sheet 4 of 9	3+000	4+000	9
6	2224-PD-HY-PP-B4-006	Al Hawasinah	HAW-CH1-FP	Sheet 5 of 9	4+000	5+000	10
7	2224-PD-HY-PP-B4-007	Al Hawasinah	HAW-CH1-FP	Sheet 6 of 9	5+000	6+000	11
8	2224-PD-HY-PP-B4-008	Al Hawasinah	HAW-CH1-FP	Sheet 7 of 9	6+000	7+000	12
9	2224-PD-HY-PP-B4-009	Al Hawasinah	HAW-CH1-FP	Sheet 8 of 9	7+000	8+000	13
10	2224-PD-HY-PP-B4-010	Al Hawasinah	HAW-CH1-FP	Sheet 9 of 9	8+000	8+203	14
11	2224-PD-HY-PP-B4-011	Al Hawasinah	HAW-CH2-SS	Key map			15
12	2224-PD-HY-PP-B4-012	Al Hawasinah	HAW-CH2-SS	Sheet 1 of 8	0+000	1+000	16
13	2224-PD-HY-PP-B4-013	Al Hawasinah	HAW-CH2-SS	Sheet 2 of 8	1+000	2+000	17
14	2224-PD-HY-PP-B4-014	Al Hawasinah	HAW-CH2-SS	Sheet 3 of 8	2+000	3+000	18
15	2224-PD-HY-PP-B4-015	Al Hawasinah	HAW-CH2-SS	Sheet 4 of 8	3+000	4+000	19
16	2224-PD-HY-PP-B4-016	Al Hawasinah	HAW-CH2-SS	Sheet 5 of 8	4+000	5+000	20
17	2224-PD-HY-PP-B4-017	Al Hawasinah	HAW-CH2-SS	Sheet 6 of 8	5+000	6+000	21
18	2224-PD-HY-PP-B4-018	Al Hawasinah	HAW-CH2-SS	Sheet 7 of 8	6+000	7+000	22
19	2224-PD-HY-PP-B4-019	Al Hawasinah	HAW-CH2-SS	Sheet 8 of 8	7+000	7+721	23
20	2224-PD-HY-PP-B4-020	Al Hawasinah	HAW-CH3-SS	Key map			24
21	2224-PD-HY-PP-B4-021	Al Hawasinah	HAW-CH3-SS	Sheet 1 of 2	0+000	1+000	25
22	2224-PD-HY-PP-B4-022	Al Hawasinah	HAW-CH3-SS	Sheet 2 of 2	1+000	1+440	26
23	2224-PD-HY-PP-B4-023	Al Hawasinah	HAW-CH4-SS	Key map			27
24	2224-PD-HY-PP-B4-024	Al Hawasinah	HAW-CH4-SS	Sheet 1 of 2	0+000	1+000	28
25	2224-PD-HY-PP-B4-025	Al Hawasinah	HAW-CH4-SS	Sheet 2 of 2	1+000	1+385	29
26	2224-PD-HY-PP-B4-026	Al Hawasinah	HAW-CH5-SS	Key map			30
27	2224-PD-HY-PP-B4-027	Al Hawasinah	HAW-CH5-SS	Sheet 1 of 8	0+000	1+000	31
28	2224-PD-HY-PP-B4-028	Al Hawasinah	HAW-CH5-SS	Sheet 2 of 8	1+000	2+000	32
29	2224-PD-HY-PP-B4-029	Al Hawasinah	HAW-CH5-SS	Sheet 3 of 8	2+000	3+000	33
30	2224-PD-HY-PP-B4-030	Al Hawasinah	HAW-CH5-SS	Sheet 4 of 8	3+000	4+000	34
31	2224-PD-HY-PP-B4-031	Al Hawasinah	HAW-CH5-SS	Sheet 5 of 8	4+000	5+000	35
32	2224-PD-HY-PP-B4-032	Al Hawasinah	HAW-CH5-SS	Sheet 6 of 8	5+000	6+000	36
33	2224-PD-HY-PP-B4-033	Al Hawasinah	HAW-CH5-SS	Sheet 7 of 8	6+000	7+000	37
34	2224-PD-HY-PP-B4-034	Al Hawasinah	HAW-CH5-SS	Sheet 8 of 8	7+000	7+065	38
35	2224-PD-HY-PP-B4-035	Al Hawasinah	HAW-CH6-SS	Key map			39
36	2224-PD-HY-PP-B4-036	Al Hawasinah	HAW-CH6-SS	Sheet 1 of 2	0+000	1+000	40
37	2224-PD-HY-PP-B4-037	Al Hawasinah	HAW-CH6-SS	Sheet 2 of 2	1+000	1+270	41
38	2224-PD-HY-PP-B4-038	Al Hawasinah	HAW-CH7-SS	Key map			42
39	2224-PD-HY-PP-B4-039	Al Hawasinah	HAW-CH7-SS	Sheet 1 of 7	0+000	1+000	43
40	2224-PD-HY-PP-B4-040	Al Hawasinah	HAW-CH7-SS	Sheet 2 of 7	1+000	2+000	44
41	2224-PD-HY-PP-B4-041	Al Hawasinah	HAW-CH7-SS	Sheet 3 of 7	2+000	3+000	45
42	2224-PD-HY-PP-B4-042	Al Hawasinah	HAW-CH7-SS	Sheet 4 of 7	3+000	4+000	46
43	2224-PD-HY-PP-B4-043	Al Hawasinah	HAW-CH7-SS	Sheet 5 of 7	4+000	5+000	47
44	2224-PD-HY-PP-B4-044	Al Hawasinah	HAW-CH7-SS	Sheet 6 of 7	5+000	6+000	48
45	2224-PD-HY-PP-B4-045	Al Hawasinah	HAW-CH7-SS	Sheet 7 of 7	6+000	6+507	49
46	2224-PD-HY-PP-B4-046	Sakhin	SAK-CH1-FP	Key map			51
47	2224-PD-HY-PP-B4-047	Sakhin	SAK-CH1-FP	Sheet 1 of 13	0+000	1+000	52
48	2224-PD-HY-PP-B4-048	Sakhin	SAK-CH1-FP	Sheet 2 of 13	1+000	2+000	53
49	2224-PD-HY-PP-B4-049	Sakhin	SAK-CH1-FP	Sheet 3 of 13	2+000	3+000	54
50	2224-PD-HY-PP-B4-050	Sakhin	SAK-CH1-FP	Sheet 4 of 13	3+000	4+000	55
51	2224-PD-HY-PP-B4-051	Sakhin	SAK-CH1-FP	Sheet 5 of 13	4+000	5+000	56
52	2224-PD-HY-PP-B4-052	Sakhin	SAK-CH1-FP	Sheet 6 of 13	5+000	6+000	57
53	2224-PD-HY-PP-B4-053	Sakhin	SAK-CH1-FP	Sheet 7 of 13	6+000	7+000	58
54	2224-PD-HY-PP-B4-054	Sakhin	SAK-CH1-FP	Sheet 8 of 13	7+000	8+000	59
55	2224-PD-HY-PP-B4-055	Sakhin	SAK-CH1-FP	Sheet 9 of 13	8+000	9+000	60
56	2224-PD-HY-PP-B4-056	Sakhin	SAK-CH1-FP	Sheet 10 of 13	9+000	10+000	61
57	2224-PD-HY-PP-B4-057	Sakhin	SAK-CH1-FP	Sheet 11 of 13	10+000	11+000	62
58	2224-PD-HY-PP-B4-058	Sakhin	SAK-CH1-FP	Sheet 12 of 13	11+000	12+000	63
59	2224-PD-HY-PP-B4-059	Sakhin	SAK-CH1-FP	Sheet 13 of 13	12+000	12+466	64
60	2224-PD-HY-PP-B4-060	Sakhin	SAK-CH2-FP	Key map			65
61	2224-PD-HY-PP-B4-061	Sakhin	SAK-CH2-FP	Sheet 1 of 10	0+000	1+000	66
62	2224-PD-HY-PP-B4-062	Sakhin	SAK-CH2-FP	Sheet 2 of 10	1+000	2+000	67
63	2224-PD-HY-PP-B4-063	Sakhin	SAK-CH2-FP	Sheet 3 of 10	2+000	3+000	68
64	2224-PD-HY-PP-B4-064	Sakhin	SAK-CH2-FP	Sheet 4 of 10	3+000	4+000	69
65	2224-PD-HY-PP-B4-065	Sakhin	SAK-CH2-FP	Sheet 5 of 10	4+000	5+000	70
66	2224-PD-HY-PP-B4-066	Sakhin	SAK-CH2-FP	Sheet 6 of 10	5+000	6+000	71
67	2224-PD-HY-PP-B4-067	Sakhin	SAK-CH2-FP	Sheet 7 of 10	6+000	7+000	72
68	2224-PD-HY-PP-B4-068	Sakhin	SAK-CH2-FP	Sheet 8 of 10	7+000	8+000	73
69	2224-PD-HY-PP-B4-069	Sakhin	SAK-CH2-FP	Sheet 9 of 10	8+000	9+000	74
70	2224-PD-HY-PP-B4-070	Sakhin	SAK-CH2-FP	Sheet 10 of 10	9+000	9+780	75
71	2224-PD-HY-PP-B4-071	Sakhin	SAK-CH3-SM	Key map			76
72	2224-PD-HY-PP-B4-072	Sakhin	SAK-CH3-SM	Sheet 1 of 7	0+000	1+000	77
73	2224-PD-HY-PP-B4-073	Sakhin	SAK-CH3-SM	Sheet 2 of 7	1+000	2+000	78
74	2224-PD-HY-PP-B4-074	Sakhin	SAK-CH3-SM	Sheet 3 of 7	2+000	3+000	79
75	2224-PD-HY-PP-B4-075	Sakhin	SAK-CH3-SM	Sheet 4 of 7	3+000	4+000	80
76	2224-PD-HY-PP-B4-076	Sakhin	SAK-CH3-SM	Sheet 5 of 7	4+000	5+000	81
77	2224-PD-HY-PP-B4-077	Sakhin	SAK-CH3-SM	Sheet 6 of 7	5+000	6+000	82
78	2224-PD-HY-PP-B4-078	Sakhin	SAK-CH3-SM	Sheet 7 of 7	6+000	6+472	83
79	2224-PD-HY-PP-B4-079	Sakhin	SAK-CH4-SS	Key map			84
80	2224-PD-HY-PP-B4-080	Sakhin	SAK-CH4-SS	Sheet 1 of 2	0+000	1+000	85
81	2224-PD-HY-PP-B4-081	Sakhin	SAK-CH4-SS	Sheet 2 of 2	1+000	1+920	86
82	2224-PD-HY-PP-B4-082	Sakhin	SAK-CH5-SS	Key map			87
83	2224-PD-HY-PP-B4-083	Sakhin	SAK-CH5-SS	Sheet 1 of 3	0+000	1+000	88
84	2224-PD-HY-PP-B4-084	Sakhin	SAK-CH5-SS	Sheet 2 of 3	1+000	2+000	89
85	2224-PD-HY-PP-B4-085	Sakhin	SAK-CH5-SS	Sheet 3 of 3	2+000	2+773	90
86	2224-PD-HY-PP-B4-086	Sarami	SAR-CH1-FP	Key map			92
87	2224-PD-HY-PP-B4-087	Sarami	SAR-CH1-FP	Sheet 1 of 18	0+000	1+000	93
88	2224-PD-HY-PP-B4-088	Sarami	SAR-CH1-FP	Sheet 2 of 18	1+000	2+000	94
89	2224-PD-HY-PP-B4-089	Sarami	SAR-CH1-FP	Sheet 3 of 18	2+000	3+000	95
90	2224-PD-HY-PP-B4-090	Sarami	SAR-CH1-FP	Sheet 4 of 18	3+000	4+000	96
91	2224-PD-HY-PP-B4-091	Sarami	SAR-CH1-FP	Sheet 5 of 18	4+000	5+000	97
92	2224-PD-HY-PP-B4-092	Sarami	SAR-CH1-FP	Sheet 6 of 18	5+000	6+000	98
93	2224-PD-HY-PP-B4-093	Sarami	SAR-CH1-FP	Sheet 7 of 18	6+000	7+000	99
94	2224-PD-HY-PP-B4-094	Sarami	SAR-CH1-FP	Sheet 8 of 18	7+000	8+000	100
95	2224-PD-HY-PP-B4-095	Sarami	SAR-CH1-FP	Sheet 9 of 18	8+000	9+000	101
96	2224-PD-HY-PP-B4-096	Sarami	SAR-CH1-FP	Sheet 10 of 18	9+000	10+000	102
97	2224-PD-HY-PP-B4-097	Sarami	SAR-CH1-FP	Sheet 11 of 18	10+000	11+000	103
98	2224-PD-HY-PP-B4-098	Sarami	SAR-CH1-FP	Sheet 12 of 18	11+000	12+000	104
99	2224-PD-HY-PP-B4-099	Sarami	SAR-CH1-FP	Sheet 13 of 18	12+000	13+000	105
100	2224-PD-HY-PP-B4-100	Sarami	SAR-CH1-FP	Sheet 14 of 18	13+000	14+000	106
101	2224-PD-HY-PP-B4-101	Sarami	SAR-CH1-FP	Sheet 15 of 18	14+000	15+000	107
102	2224-PD-HY-PP-B4-102	Sarami	SAR-CH1-FP	Sheet 16 of 18	15+000	16+000	108
103	2224-PD-HY-PP-B4-103	Sarami	SAR-CH1-FP	Sheet 17 of 18	16+000	17+000	109
104	2224-PD-HY-PP-B4-104	Sarami	SAR-CH1-FP	Sheet 18 of 18	17+000	17+552	110
105	2224-PD-HY-PP-B4-105	Sarami	SAR-CH2-SM	Key map			111
106	2224-PD-HY-PP-B4-106	Sarami	SAR-CH2-SM	Sheet 1 of 7	0+000	1+000	112
107	2224-PD-HY-PP-B4-107	Sarami	SAR-CH2-SM	Sheet 2 of 7	1+000	2+000	113
108	2224-PD-HY-PP-B4-108	Sarami	SAR-CH2-SM	Sheet 3 of 7	2+000	3+000	114
109	2224-PD-HY-PP-B4-109	Sarami	SAR-CH2-SM	Sheet 4 of 7	3+000	4+000	115
110	2224-PD-HY-PP-B4-110	Sarami	SAR-CH2-SM	Sheet 5 of 7	4+000	5+000	116
111	2224-PD-HY-PP-B4-111	Sarami	SAR-CH2-SM	Sheet 6 of 7	5+000	6+000	117
112	2224-PD-HY-PP-B4-112	Sarami	SAR-CH2-SM	Sheet 7 of 7	6+000	6+142	118
113	2224-PD-HY-PP-B4-113	Sarami	SAR-CH3-SS	Key map			119
114	2224-PD-HY-PP-B4-114	Sarami	SAR-CH3-SS	Sheet 1 of 7	0+000	1+000	120
115	2224-PD-HY-PP-B4-115	Sarami	SAR-CH3-SS	Sheet 2 of 7	1+000	2+000	121
116	2224-PD-HY-PP-B4-116	Sarami	SAR-CH3-SS	Sheet 3 of 7	2+000	3+000	122
117	2224-PD-HY-PP-B4-117	Sarami	SAR-CH3-SS	Sheet 4 of 7	3+000	4+000	123
118	2224-PD-HY-PP-B4-118	Sarami	SAR-CH3-SS	Sheet 5 of 7	4+000	5+000	124
119	2224-PD-HY-PP-B4-119	Sarami	SAR-CH3-SS	Sheet 6 of 7	5+000	6+000	125
120	2224-PD-HY-PP-B4-120	Sarami	SAR-CH3-SS	Sheet 7 of 7	6+000	6+865	126
121	2224-PD-HY-PP-B4-121	Sarami	SAR-CH4-SS	Key map			127
122	2224-PD-HY-PP-B4-122	Sarami	SAR-CH4-SS	Sheet 1 of 4	0+000	1+000	128
123	2224-PD-HY-PP-B4-123	Sarami	SAR-CH4-SS	Sheet 2 of 4	1+000	2+000	129
124	2224-PD-HY-PP-B4-124	Sarami	SAR-CH4-SS	Sheet 3 of 4	2+000	3+000	130
125	2224-PD-HY-PP-B4-125	Sarami	SAR-CH4-SS	Sheet 4 of 4	3+000	3+104	131
126	2224-PD-HY-PP-B4-126	Shafan	SHA-CH1-FP	Key map			133
127	2224-PD-HY-PP-B4-127	Shafan	SHA-CH1-FP	Sheet 1 of 9	0+000	1+000	134
128	2224-PD-HY-PP-B4-128	Shafan	SHA-CH1-FP	Sheet 2 of 9	1+000	2+000	135
129	2224-PD-HY-PP-B4-129	Shafan	SHA-CH1-FP	Sheet 3 of 9	2+000	3+000	136
130	2224-PD-HY-PP-B4-130	Shafan	SHA-CH1-FP	Sheet 4 of 9	3+000	4+000	137
131	2224-PD-HY-PP-B4-131	Shafan	SHA-CH1-FP	Sheet 5 of 9	4+000	5+000	138
132	2224-PD-HY-PP-B4-132	Shafan	SHA-CH1-FP	Sheet 6 of 9	5+000	6+000	139
133	2224-PD-HY-PP-B4-133	Shafan	SHA-CH1-FP	Sheet 7 of 9	6+000	7+000	140
134	2224-PD-HY-PP-B4-134	Shafan	SHA-CH1-FP	Sheet 8 of 9	7+000	8+000	141
135	2224-PD-HY-PP-B4-135	Shafan	SHA-CH1-FP	Sheet 9 of 9	8+000	8+044	142
136	2224-PD-HY-PP-B4-136	Shafan	SHA-CH2-SM	Key map			143
137	2224-PD-HY-PP-B4-137	Shafan	SHA-CH2-SM	Sheet 1 of 12	0+000	1+000	144
138	2224-PD-HY-PP-B4-138	Shafan	SHA-CH2-SM	Sheet 2 of 12	1+000	2+000	145
139	2224-PD-HY-PP-B4-139	Shafan	SHA-CH2-SM	Sheet 3 of 12	2+000	3+000	146
140	2224-PD-HY-PP-B4-140	Shafan	SHA-CH2-SM	Sheet 4 of 12	3+000	4+000	147
141	2224-PD-HY-PP-B4-141	Shafan	SHA-CH2-SM	Sheet 5 of 12	4+000	5+000	148
142	2224-PD-HY-PP-B4-142	Shafan	SHA-CH2-SM	Sheet 6 of 12	5+000	6+000	149
143	2224-PD-HY-PP-B4-143	Shafan	SHA-CH2-SM	Sheet 7 of 12	6+000	7+000	150
144	2224-PD-HY-PP-B4-144	Shafan	SHA-CH2-SM	Sheet 8 of 12	7+000	8+000	151
145	2224-PD-HY-PP-B4-145	Shafan	SHA-CH2-SM	Sheet 9 of 12	8+000	9+000	152
146	2224-PD-HY-PP-B4-146	Shafan	SHA-CH2-SM	Sheet 10 of 12	9+000	10+000	153
147	2224-PD-HY-PP-B4-147	Shafan	SHA-CH2-SM	Sheet 11 of 12	10+000	11+000	154
148	2224-PD-HY-PP-B4-148	Shafan	SHA-CH2-SM	Sheet 12 of 12	11+000	11+435	155
149	2224-PD-HY-PP-B4-149	Shafan	SHA-CH3-SM	Key map			156
150	2224-PD-HY-PP-B4-150	Shafan	SHA-CH3-SM	Sheet 1 of 14	0+000	1+000	157
151	2224-PD-HY-PP-B4-151	Shafan	SHA-CH3-SM	Sheet 2 of 14	1+000	2+000	158
152	2224-PD-HY-PP-B4-152	Shafan	SHA-CH3-SM	Sheet 3 of 14	2+000	3+000	159

TABLE OF DRAWINGS (continued)


No.	Drawing No.	Catchment	Channel	Drawing	Station from	Station to	Page
153	2224-PD-HY-PP-B4-153	Shafan	SHA-CH3-SM	Sheet 4 of 14	3+000	4+000	160
154	2224-PD-HY-PP-B4-154	Shafan	SHA-CH3-SM	Sheet 5 of 14	4+000	5+000	161
155	2224-PD-HY-PP-B4-155	Shafan	SHA-CH3-SM	Sheet 6 of 14	5+000	6+000	162
156	2224-PD-HY-PP-B4-156	Shafan	SHA-CH3-SM	Sheet 7 of 14	6+000	7+000	163
157	2224-PD-HY-PP-B4-157	Shafan	SHA-CH3-SM	Sheet 8 of 14	7+000	8+000	164
158	2224-PD-HY-PP-B4-158	Shafan	SHA-CH3-SM	Sheet 9 of 14	8+000	9+000	165
159	2224-PD-HY-PP-B4-159	Shafan	SHA-CH3-SM	Sheet 10 of 14	9+000	10+000	166
160	2224-PD-HY-PP-B4-160	Shafan	SHA-CH3-SM	Sheet 11 of 14	10+000	11+000	167
161	2224-PD-HY-PP-B4-161	Shafan	SHA-CH3-SM	Sheet 12 of 14	11+000	12+000	168
162	2224-PD-HY-PP-B4-162	Shafan	SHA-CH3-SM	Sheet 13 of 14	12+000	13+000	169
163	2224-PD-HY-PP-B4-163	Shafan	SHA-CH3-SM	Sheet 14 of 14	13+000	13+878	170
164	2224-PD-HY-PP-B4-164	Shafan	SHA-CH4-SM	Key map			171
165	2224-PD-HY-PP-B4-165	Shafan	SHA-CH4-SM	Sheet 1 of 9	0+000	1+000	172
166	2224-PD-HY-PP-B4-166	Shafan	SHA-CH4-SM	Sheet 2 of 9	1+000	2+000	173
167	2224-PD-HY-PP-B4-167	Shafan	SHA-CH4-SM	Sheet 3 of 9	2+000	3+000	174
168	2224-PD-HY-PP-B4-168	Shafan	SHA-CH4-SM	Sheet 4 of 9	3+000	4+000	175
169	2224-PD-HY-PP-B4-169	Shafan	SHA-CH4-SM	Sheet 5 of 9	4+000	5+000	176
170	2224-PD-HY-PP-B4-170	Shafan	SHA-CH4-SM	Sheet 6 of 9	5+000	6+000	177
171	2224-PD-HY-PP-B4-171	Shafan	SHA-CH4-SM	Sheet 7 of 9	6+000	7+000	178
172	2224-PD-HY-PP-B4-172	Shafan	SHA-CH4-SM	Sheet 8 of 9	7+000	8+000	179
173	2224-PD-HY-PP-B4-173	Shafan	SHA-CH4-SM	Sheet 9 of 9	8+000	8+276	180
174	2224-PD-HY-PP-B4-174	Shafan	SHA-CH5-SM	Key map			181
175	2224-PD-HY-PP-B4-175	Shafan	SHA-CH5-SM	Sheet 1 of 10	0+000	1+000	182
176	2224-PD-HY-PP-B4-176	Shafan	SHA-CH5-SM	Sheet 2 of 10	1+000	2+000	183
177	2224-PD-HY-PP-B4-177	Shafan	SHA-CH5-SM	Sheet 3 of 10	2+000	3+000	184
178	2224-PD-HY-PP-B4-178	Shafan	SHA-CH5-SM	Sheet 4 of 10	3+000	4+000	185
179	2224-PD-HY-PP-B4-179	Shafan	SHA-CH5-SM	Sheet 5 of 10	4+000	5+000	186
180	2224-PD-HY-PP-B4-180	Shafan	SHA-CH5-SM	Sheet 6 of 10	5+000	6+000	187
181	2224-PD-HY-PP-B4-181	Shafan	SHA-CH5-SM	Sheet 7 of 10	6+000	7+000	188
182	2224-PD-HY-PP-B4-182	Shafan	SHA-CH5-SM	Sheet 8 of 10	7+000	8+000	189
183	2224-PD-HY-PP-B4-183	Shafan	SHA-CH5-SM	Sheet 9 of 10	8+000	9+000	190
184	2224-PD-HY-PP-B4-184	Shafan	SHA-CH5-SM	Sheet 10 of 10	9+000	9+916	191
185	2224-PD-HY-PP-B4-185	Shafan	SHA-CH6-SM	Key map			192
186	2224-PD-HY-PP-B4-186	Shafan	SHA-CH6-SM	Sheet 1 of 6	0+000	1+000	193
187	2224-PD-HY-PP-B4-187	Shafan	SHA-CH6-SM	Sheet 2 of 6	1+000	2+000	194
188	2224-PD-HY-PP-B4-188	Shafan	SHA-CH6-SM	Sheet 3 of 6	2+000	3+000	195
189	2224-PD-HY-PP-B4-189	Shafan	SHA-CH6-SM	Sheet 4 of 6	3+000	4+000	196
190	2224-PD-HY-PP-B4-190	Shafan	SHA-CH6-SM	Sheet 5 of 6	4+000	5+000	197
191	2224-PD-HY-PP-B4-191	Shafan	SHA-CH6-SM	Sheet 6 of 6	5+000	5+159	198
192	2224-PD-HY-PP-B4-192	Shafan	SHA-CH7-SM	Key map			199
193	2224-PD-HY-PP-B4-193	Shafan	SHA-CH7-SM	Sheet 1 of 8	0+000	1+000	200
194	2224-PD-HY-PP-B4-194	Shafan	SHA-CH7-SM	Sheet 2 of 8	1+000	2+000	201
195	2224-PD-HY-PP-B4-195	Shafan	SHA-CH7-SM	Sheet 3 of 8	2+000	3+000	202
196	2224-PD-HY-PP-B4-196	Shafan	SHA-CH7-SM	Sheet 4 of 8	3+000	4+000	203
197	2224-PD-HY-PP-B4-197	Shafan	SHA-CH7-SM	Sheet 5 of 8	4+000	5+000	204
198	2224-PD-HY-PP-B4-198	Shafan	SHA-CH7-SM	Sheet 6 of 8	5+000	6+000	205
199	2224-PD-HY-PP-B4-199	Shafan	SHA-CH7-SM	Sheet 7 of 8	6+000	7+000	206
200	2224-PD-HY-PP-B4-200	Shafan	SHA-CH7-SM	Sheet 8 of 8	7+000	7+405	207
201	2224-PD-HY-PP-B4-201	Shafan	SHA-CH8-SS	Key map			208
202	2224-PD-HY-PP-B4-202	Shafan	SHA-CH8-SS	Sheet 1 of 6	0+000	1+000	209
203	2224-PD-HY-PP-B4-203	Shafan	SHA-CH8-SS	Sheet 2 of 6	1+000	2+000	210
204	2224-PD-HY-PP-B4-204	Shafan	SHA-CH8-SS	Sheet 3 of 6	2+000	3+000	211
205	2224-PD-HY-PP-B4-205	Shafan	SHA-CH8-SS	Sheet 4 of 6	3+000	4+000	212
206	2224-PD-HY-PP-B4-206	Shafan	SHA-CH8-SS	Sheet 5 of 6	4+000	5+000	213
207	2224-PD-HY-PP-B4-207	Shafan	SHA-CH8-SS	Sheet 6 of 6	5+000	5+884	214
208	2224-PD-HY-PP-B4-208	Shafan	SHA-CH9-SS	Key map			215
209	2224-PD-HY-PP-B4-209	Shafan	SHA-CH9-SS	Sheet 1 of 6	0+000	1+000	216
210	2224-PD-HY-PP-B4-210	Shafan	SHA-CH9-SS	Sheet 2 of 6	1+000	2+000	217
211	2224-PD-HY-PP-B4-211	Shafan	SHA-CH9-SS	Sheet 3 of 6	2+000	3+000	218
212	2224-PD-HY-PP-B4-212	Shafan	SHA-CH9-SS	Sheet 4 of 6	3+000	4+000	219
213	2224-PD-HY-PP-B4-213	Shafan	SHA-CH9-SS	Sheet 5 of 6	4+000	5+000	220
214	2224-PD-HY-PP-B4-214	Shafan	SHA-CH9-SS	Sheet 6 of 6	5+000	5+489	221
215	2224-PD-HY-PP-B4-215	Shafan	SHA-CH10-SS	Key map			222
216	2224-PD-HY-PP-B4-216	Shafan	SHA-CH10-SS	Sheet 1 of 6	0+000	1+000	223
217	2224-PD-HY-PP-B4-217	Shafan	SHA-CH10-SS	Sheet 2 of 6	1+000	2+000	224
218	2224-PD-HY-PP-B4-218	Shafan	SHA-CH10-SS	Sheet 3 of 6	2+000	3+000	225
219	2224-PD-HY-PP-B4-219	Shafan	SHA-CH10-SS	Sheet 4 of 6	3+000	4+000	226
220	2224-PD-HY-PP-B4-220	Shafan	SHA-CH10-SS	Sheet 5 of 6	4+000	5+000	227
221	2224-PD-HY-PP-B4-221	Shafan	SHA-CH10-SS	Sheet 6 of 6	5+000	5+374	228
222	2224-PD-HY-PP-B4-222	Shafan	SHA-CH11-SS	Key map			229
223	2224-PD-HY-PP-B4-223	Shafan	SHA-CH11-SS	Sheet 1 of 3	0+000	1+000	230
224	2224-PD-HY-PP-B4-224	Shafan	SHA-CH11-SS	Sheet 2 of 3	1+000	2+000	231
225	2224-PD-HY-PP-B4-225	Shafan	SHA-CH11-SS	Sheet 3 of 3	2+000	2+427	232
226	2224-PD-HY-PP-B4-226	Shafan	SHA-CH12-SS	Key map			233
227	2224-PD-HY-PP-B4-227	Shafan	SHA-CH12-SS	Sheet 1 of 4	0+000	1+000	234
228	2224-PD-HY-PP-B4-228	Shafan	SHA-CH12-SS	Sheet 2 of 4	1+000	2+000	235
229	2224-PD-HY-PP-B4-229	Shafan	SHA-CH12-SS	Sheet 3 of 4	2+000	3+000	236
230	2224-PD-HY-PP-B4-230	Shafan	SHA-CH12-SS	Sheet 4 of 4	3+000	3+773	237
231	2224-PD-HY-PP-B4-231	Shafan	SHA-CH13-SS	Key map			238
232	2224-PD-HY-PP-B4-232	Shafan	SHA-CH13-SS	Sheet 1 of 2	0+000	1+000	239
233	2224-PD-HY-PP-B4-233	Shafan	SHA-CH13-SS	Sheet 2 of 2	1+000	1+642	240
234	2224-PD-HY-PP-B4-234	Shafan	SHA-CH14-SS	Key map			241
235	2224-PD-HY-PP-B4-235	Shafan	SHA-CH14-SS	Sheet 1 of 4	0+000	1+000	242
236	2224-PD-HY-PP-B4-236	Shafan	SHA-CH14-SS	Sheet 2 of 4	1+000	2+000	243
237	2224-PD-HY-PP-B4-237	Shafan	SHA-CH14-SS	Sheet 3 of 4	2+000	3+000	244
238	2224-PD-HY-PP-B4-238	Shafan	SHA-CH14-SS	Sheet 4 of 4	3+000	3+944	245
239	2224-PD-HY-PP-B4-239	Shafan	SHA-CH15-SS	Key map			246
240	2224-PD-HY-PP-B4-240	Shafan	SHA-CH15-SS	Sheet 1 of 7	0+000	1+000	247
241	2224-PD-HY-PP-B4-241	Shafan	SHA-CH15-SS	Sheet 2 of 7	1+000	2+000	248
242	2224-PD-HY-PP-B4-242	Shafan	SHA-CH15-SS	Sheet 3 of 7	2+000	3+000	249
243	2224-PD-HY-PP-B4-243	Shafan	SHA-CH15-SS	Sheet 4 of 7	3+000	4+000	250
244	2224-PD-HY-PP-B4-244	Shafan	SHA-CH15-SS	Sheet 5 of 7	4+000	5+000	251
245	2224-PD-HY-PP-B4-245	Shafan	SHA-CH15-SS	Sheet 6 of 7	5+000	6+000	252
246	2224-PD-HY-PP-B4-246	Shafan	SHA-CH15-SS	Sheet 7 of 7	6+000	6+807	253
247	2224-PD-HY-PP-B4-247	Shafan	SHA-CH16-SS	Key map			254
248	2224-PD-HY-PP-B4-248	Shafan	SHA-CH16-SS	Sheet 1 of 7	0+000	1+000	255
249	2224-PD-HY-PP-B4-249	Shafan	SHA-CH16-SS	Sheet 2 of 7	1+000	2+000	256
250	2224-PD-HY-PP-B4-250	Shafan	SHA-CH16-SS	Sheet 3 of 7	2+000	3+000	257
251	2224-PD-HY-PP-B4-251	Shafan	SHA-CH16-SS	Sheet 4 of 7	3+000	4+000	258
252	2224-PD-HY-PP-B4-252	Shafan	SHA-CH16-SS	Sheet 5 of 7	4+000	5+000	259
253	2224-PD-HY-PP-B4-253	Shafan	SHA-CH16-SS	Sheet 6 of 7	5+000	6+000	260
254	2224-PD-HY-PP-B4-254	Shafan	SHA-CH16-SS	Sheet 7 of 7	6+000	6+425	261
255	2224-PD-HY-PP-B4-255	Shafan	SHA-CH17-SS	Key map			262
256	2224-PD-HY-PP-B4-256	Shafan	SHA-CH17-SS	Sheet 1 of 6	0+000	1+000	263
257	2224-PD-HY-PP-B4-257	Shafan	SHA-CH17-SS	Sheet 2 of 6	1+000	2+000	264
258	2224-PD-HY-PP-B4-258	Shafan	SHA-CH17-SS	Sheet 3 of 6	2+000	3+000	265
259	2224-PD-HY-PP-B4-259	Shafan	SHA-CH17-SS	Sheet 4 of 6	3+000	4+000	266
260	2224-PD-HY-PP-B4-260	Shafan	SHA-CH17-SS	Sheet 5 of 6	4+000	5+000	267
261	2224-PD-HY-PP-B4-261	Shafan	SHA-CH17-SS	Sheet 6 of 6	5+000	5+107	268
262	2224-PD-HY-PP-B4-262	Shafan	SHA-CH18-SS	Key map			269
263	2224-PD-HY-PP-B4-263	Shafan	SHA-CH18-SS	Sheet 1 of 4	0+000	1+000	270
264	2224-PD-HY-PP-B4-264	Shafan	SHA-CH18-SS	Sheet 2 of 4	1+000	2+000	271
265	2224-PD-HY-PP-B4-265	Shafan	SHA-CH18-SS	Sheet 3 of 4	2+000	3+000	272
266	2224-PD-HY-PP-B4-266	Shafan	SHA-CH18-SS	Sheet 4 of 4	3+000	3+019	273
267	2224-PD-HY-PP-B4-267	Shafan	SHA-CH19-SS	Key map			274
268	2224-PD-HY-PP-B4-268	Shafan	SHA-CH19-SS	Sheet 1 of 2	0+000	1+000	275
269	2224-PD-HY-PP-B4-269	Shafan	SHA-CH19-SS	Sheet 2 of 2	1+000	1+811	276
270	2224-PD-HY-PP-B4-270	Shafan	SHA-CH20-SS	Key map			277
271	2224-PD-HY-PP-B4-271	Shafan	SHA-CH20-SS	Sheet 1 of 4	0+000	1+000	278
272	2224-PD-HY-PP-B4-272	Shafan	SHA-CH20-SS	Sheet 2 of 4	1+000	2+000	279
273	2224-PD-HY-PP-B4-273	Shafan	SHA-CH20-SS	Sheet 3 of 4	2+000	3+000	280
274	2224-PD-HY-PP-B4-274	Shafan	SHA-CH20-SS	Sheet 4 of 4	3+000	3+755	281
275	2224-PD-HY-PP-B4-275	Shafan	SHA-CH21-SS	Key map			282
276	2224-PD-HY-PP-B4-276	Shafan	SHA-CH21-SS	Sheet 1 of 2	0+000	1+000	283
277	2224-PD-HY-PP-B4-277	Shafan	SHA-CH21-SS	Sheet 2 of 2	1+000	1+088	284

PLAN AND PROFILE DRAWINGS

AL HAWASINAH

Al Hawasinah catchment 7 channels

HAW-CH1-FP	drawings 2224-PD-HY-PP-B4-001 to 2224-PD-HY-PP-B4-010	pages 5 to 14
HAW-CH2-SS	drawings 2224-PD-HY-PP-B4-011 to 2224-PD-HY-PP-B4-019	pages 15 to 23
HAW-CH3-SS	drawings 2224-PD-HY-PP-B4-020 to 2224-PD-HY-PP-B4-022	pages 24 to 26
HAW-CH4-SS	drawings 2224-PD-HY-PP-B4-023 to 2224-PD-HY-PP-B4-025	pages 27 to 29
HAW-CH5-SS	drawings 2224-PD-HY-PP-B4-026 to 2224-PD-HY-PP-B4-034	pages 30 to 38
HAW-CH6-SS	drawings 2224-PD-HY-PP-B4-035 to 2224-PD-HY-PP-B4-037	pages 39 to 41
HAW-CH7-SS	drawings 2224-PD-HY-PP-B4-038 to 2224-PD-HY-PP-B4-045	pages 42 to 49

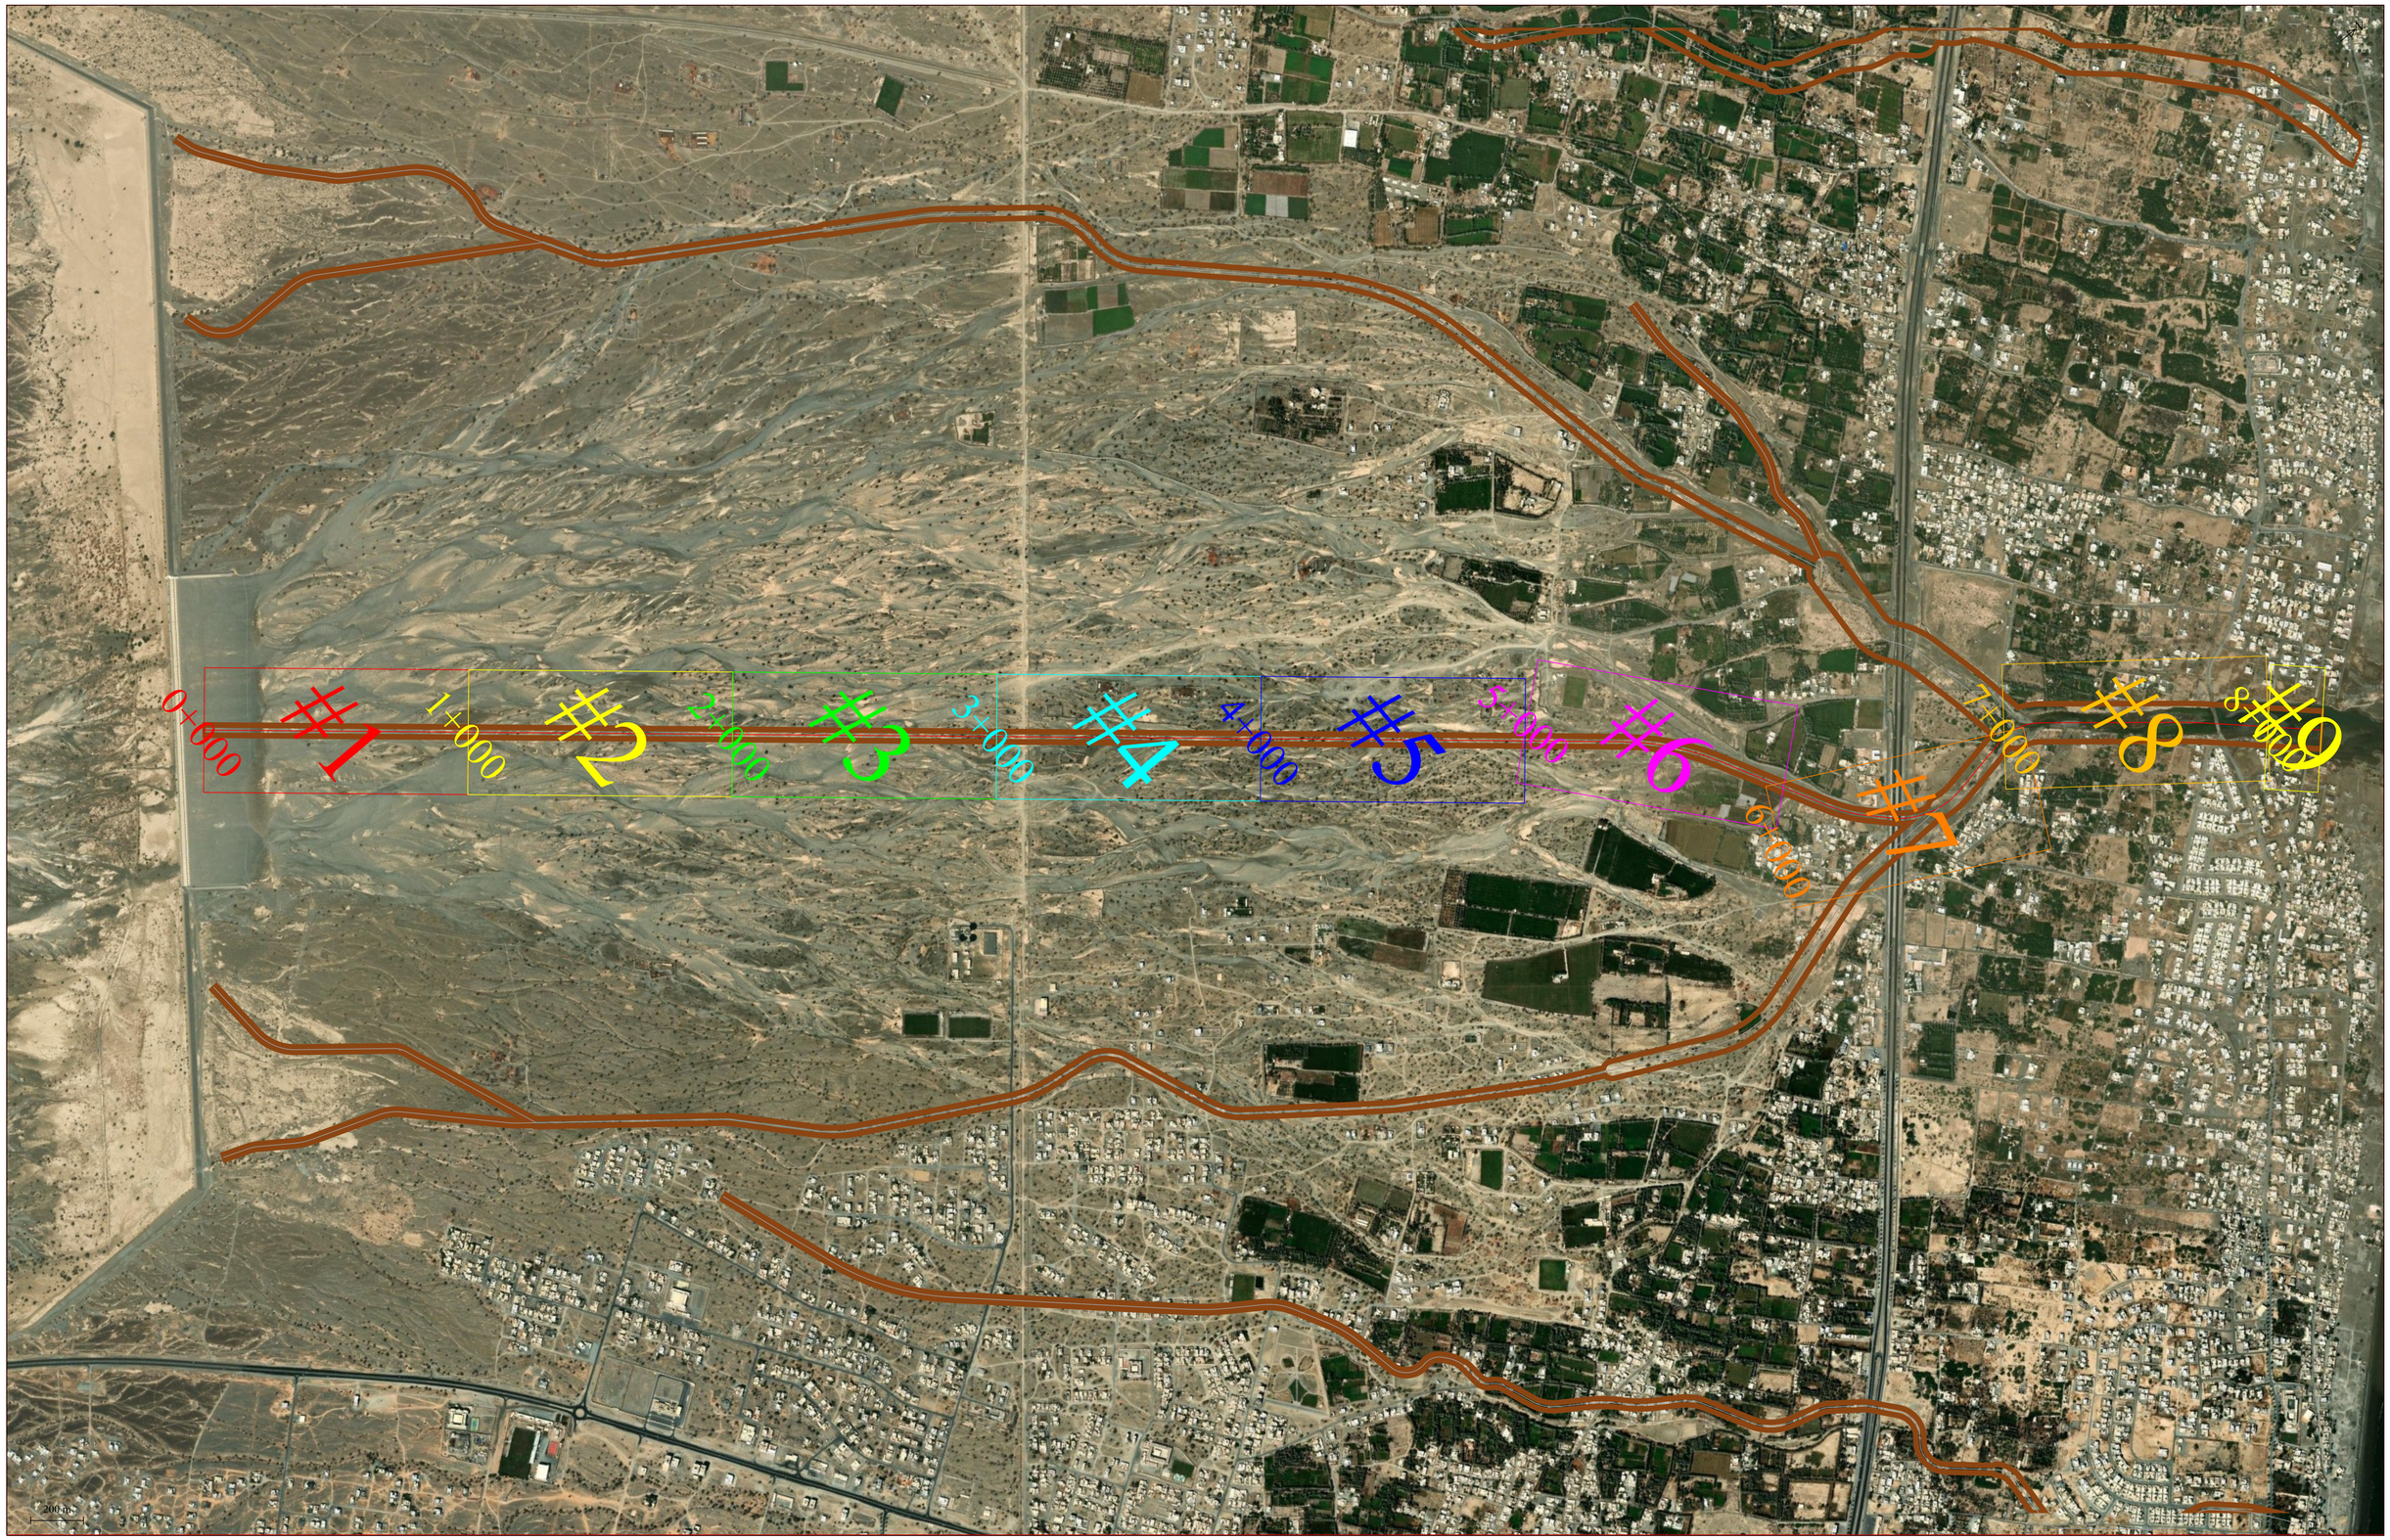

CLIENT:

Sultanate of Oman
MINISTRY OF AGRICULTURE, FISHERIES
WEALTH AND WATER RESOURCES

CONSULTANT:

RENARDET S.A. & PARTNERS
Consulting Engineers LLC.

PROJECT NAME:

FLOOD PROTECTION SCHEME IN NORTH AND SOUTH AL BATINAH GOVERNORATES
Block 04

DRAWING TITLE:

Flood Protection Channel
Key Map - HAW-CH1-FP (9 sheets)

NO	REVISION DESCRIPTION	DRAWN	DESIGNED	CHECKED	APPROVED	DATE
1			M.Keivanlou	M.Keivanlou	A.Tabatabaei	11.10.2026

DRAWN:
DESIGNED: M.Keivanlou
CHECKED: M.Keivanlou
APPROVED: A.Tabatabaei

DRAWING NO: 2224-PD-HY-PP-B4-001
SCALE: 1:12500
DATE: 11.10.2026
REVISION: 1