
SHAFAN CATCHMENT — KEY PLAN

Channels and dykes with their names, their extents (designed bed in yellow, corridor with the embankments and access roads in brown) and the stations every 1000 m; dam axes in magenta

2224-PD-HY-PP-B4 Revision 1 13.10.2026

Plan and profile drawings of the flood protection channels — Shafan catchment

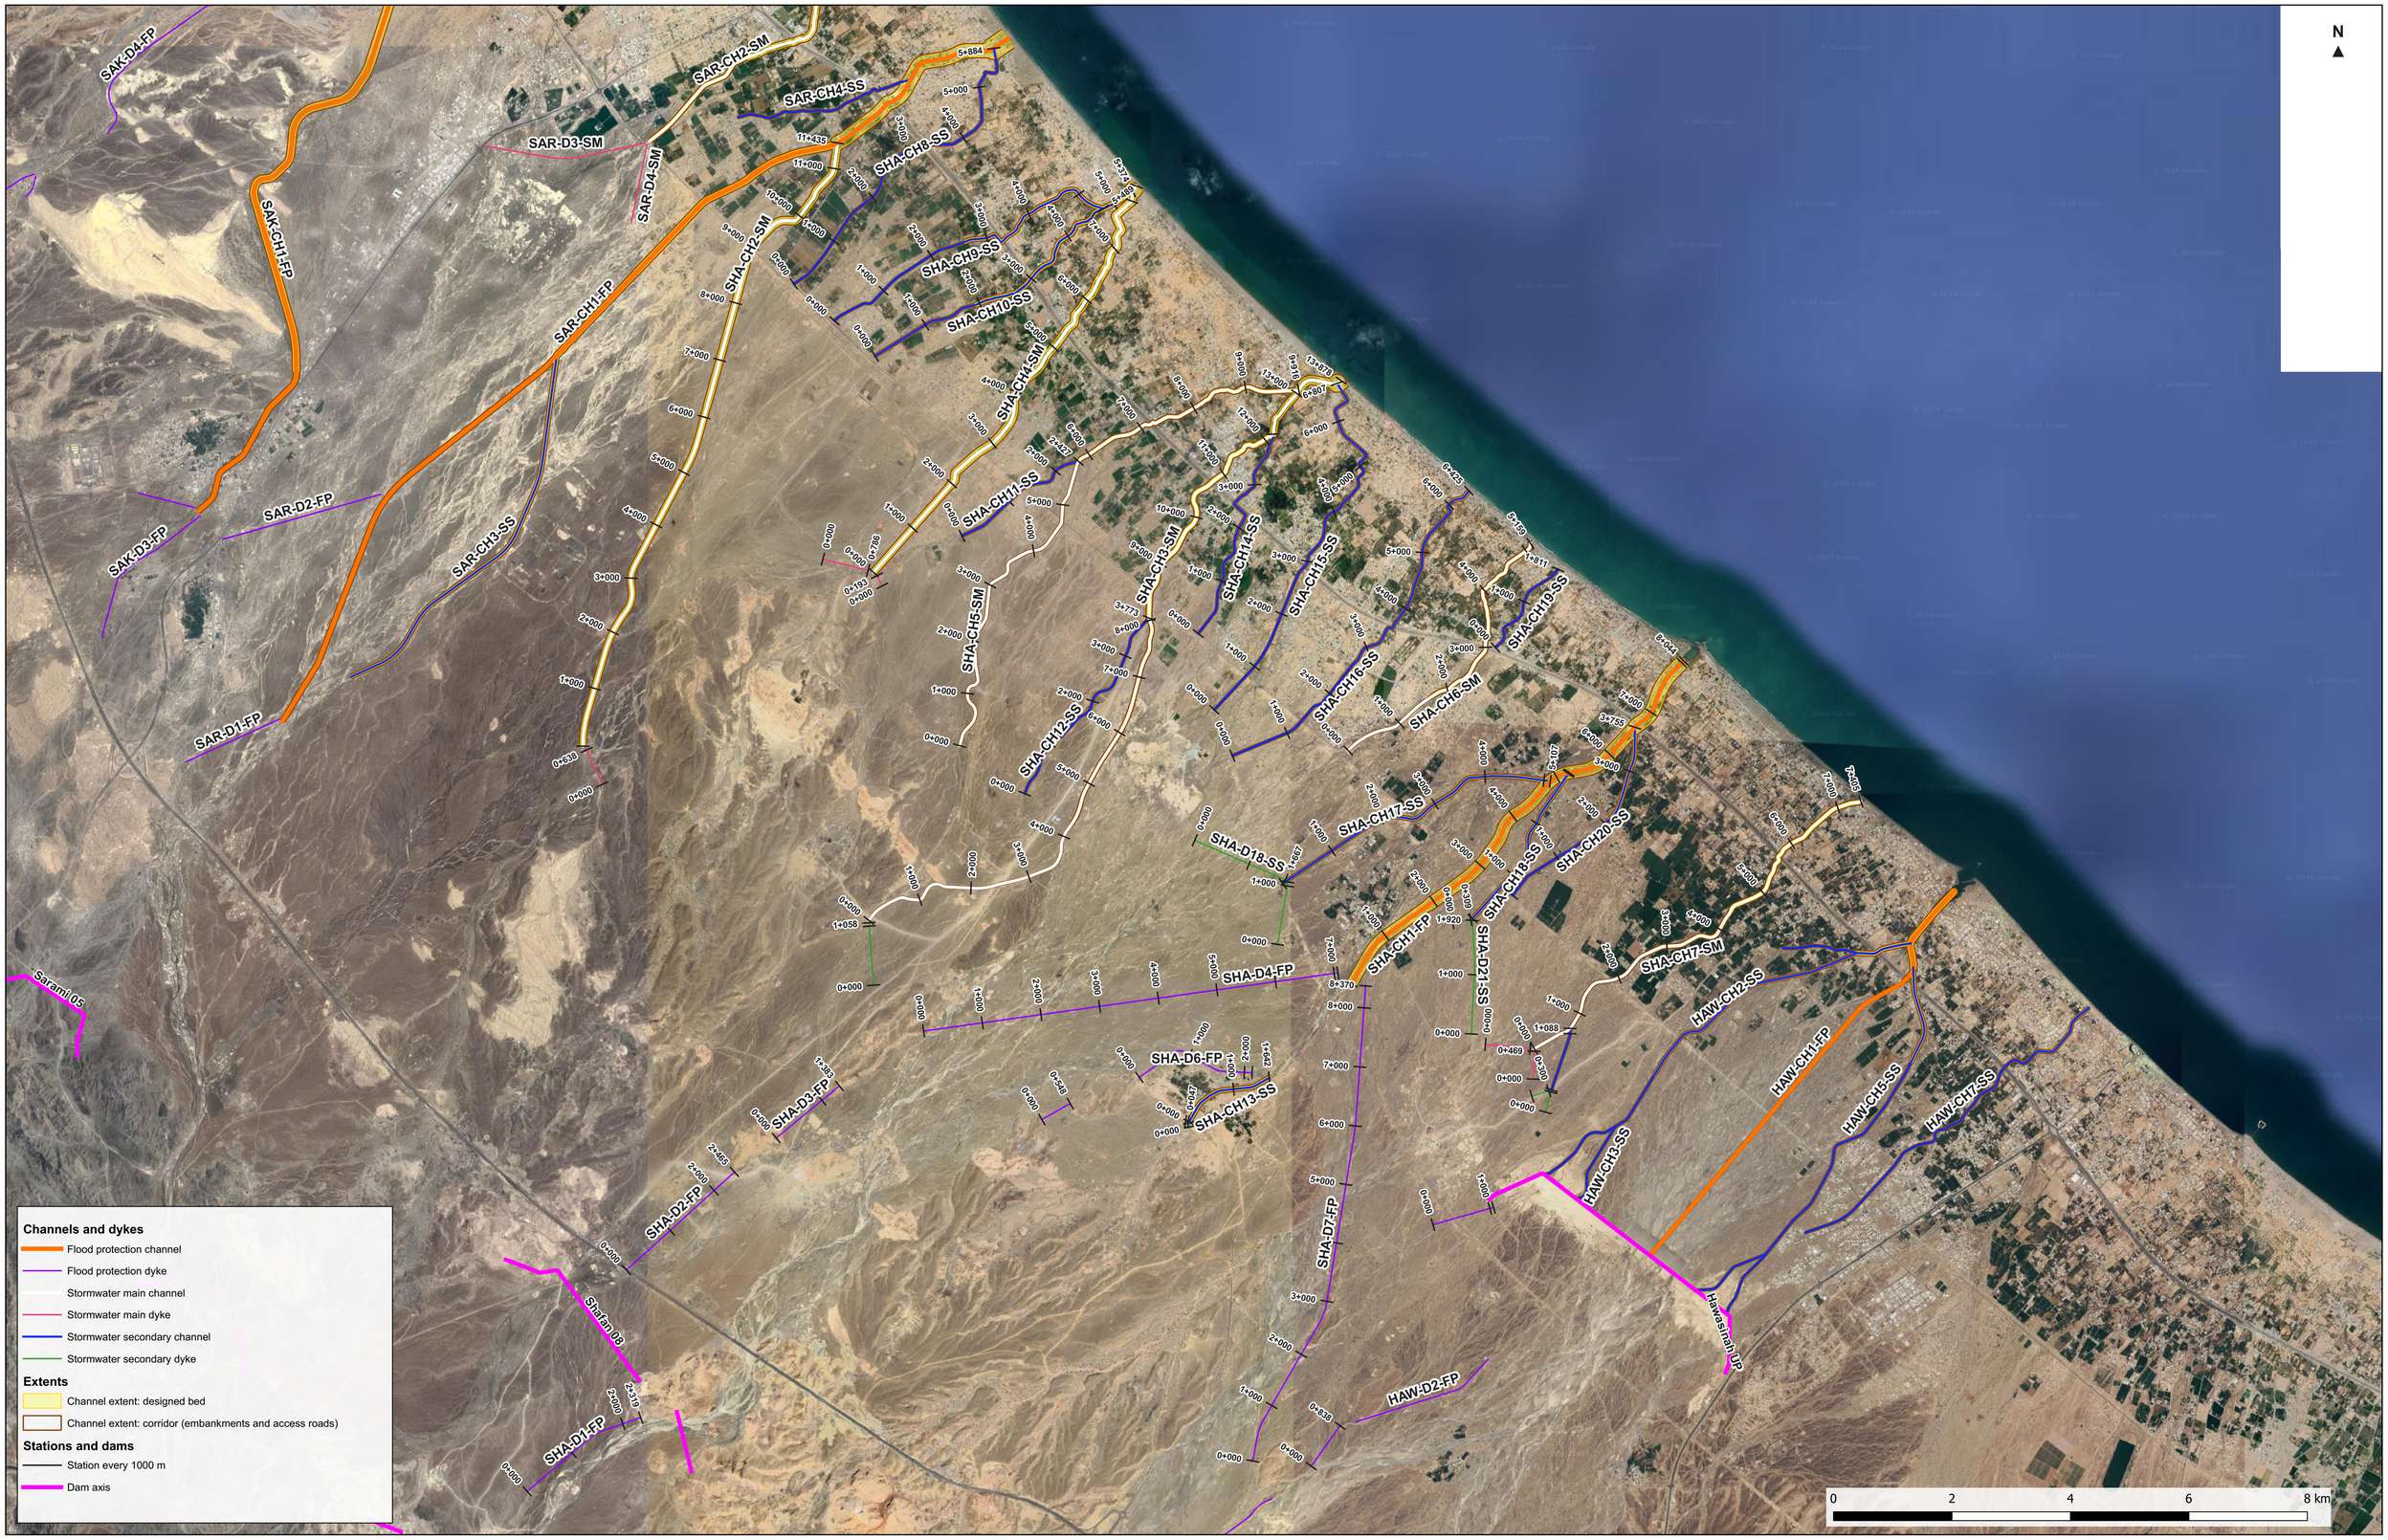

Scale 1:49 500 (A1) Background: Google satellite image Coordinates: WGS 84 / UTM zone 40N